

ÁREAS DE TRABAJO · EDIFICIO A

Laboratorio típico 85 m² · 16 WA dobles · 32 puertos RJ45 Cat 6A · planta y mobiliario supuestos

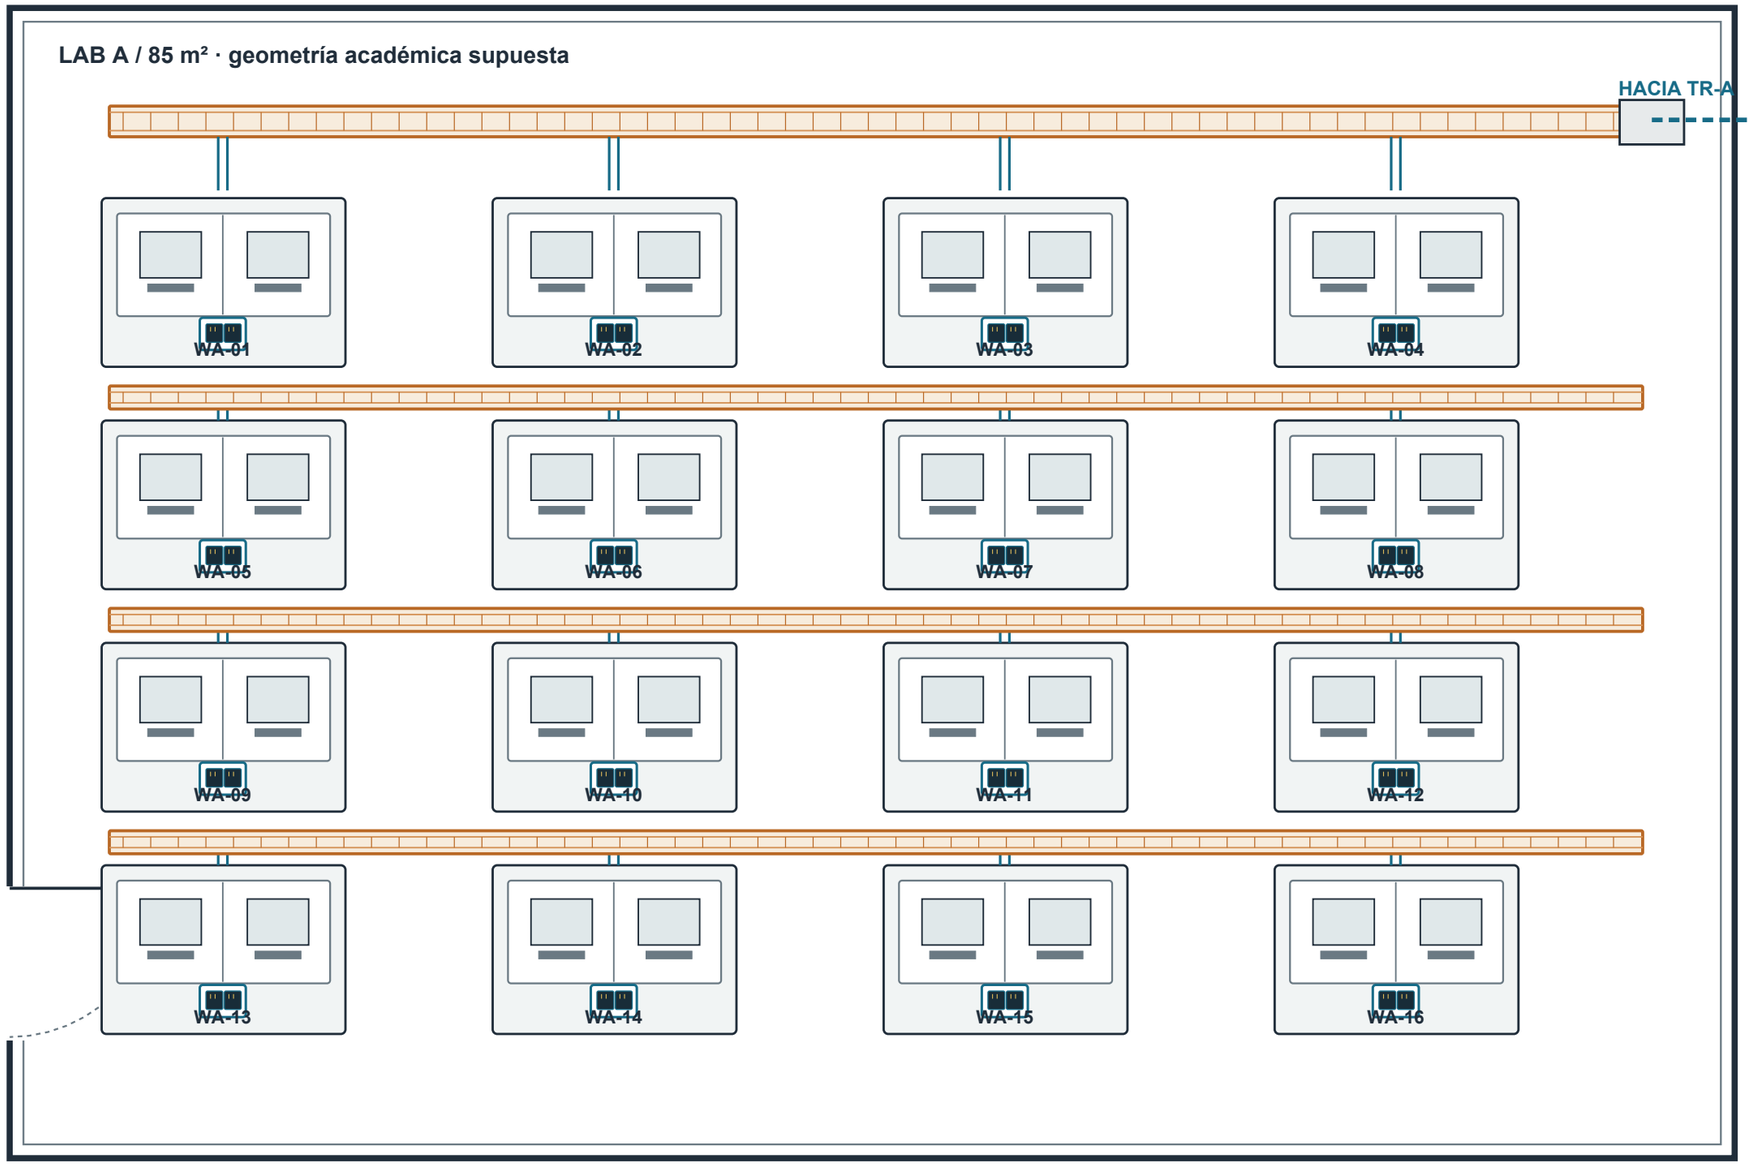

16 placas dobles identificadas WA-01–WA-16; cada símbolo muestra 2 bocas RJ45; 32 enlaces permanentes Cat 6A.

DETALLE · PUESTO DOBLE

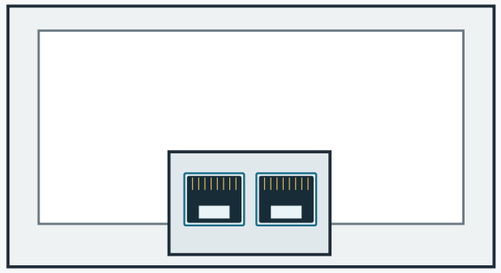

Placa, caja y conectores ilustrativos.

2 cables Cat 6A por WA; ruta agrupada.

RUTA Y LEYENDA

- Bandeja de distribución*
- Tubería nominal Ø25*
- WA doble · 2 × RJ45
- Cat 6A permanente

Ruta agrupada hacia TR; no se dibujan 32 cables individuales superpuestos.

* Posición y recorrido supuestos.

Escala: esquemático, sin escala.

PROYECTO: INA CENATE | ELTT12000 | CABLEADO ESTRUCTURADO	FECHA 2026-10-29	REV. C	LÁMINA 04/09
16 WA dobles × 2 RJ45 = 32 salidas por laboratorio. Mobiliario y canalizaciones supuestos.	SIN ESCALA	IA: apoyo visual	NO CONSTRUCTIVO