

BACKBONE EXTERIOR · TRES EDIFICIOS

ER principal existente · ER-A · ER-B | E1 / E2 / E3: cable OS2 24F | recorridos de escenario

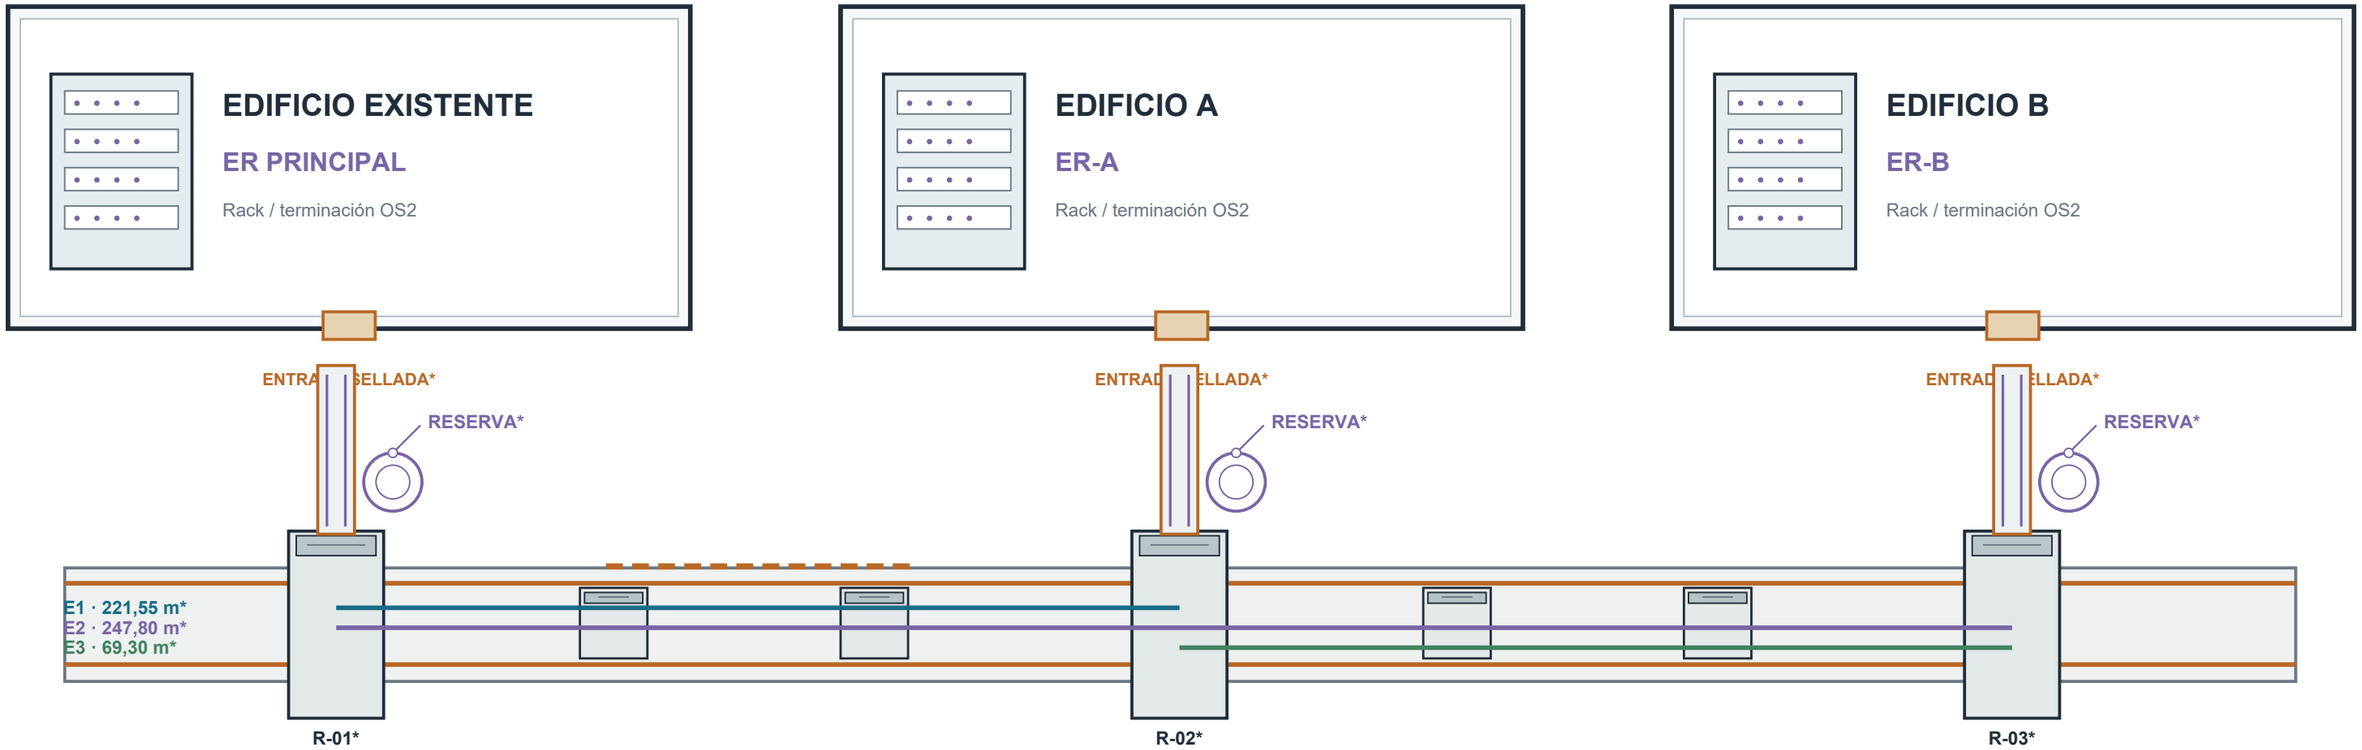

CORTE Y SÍMBOLOS DE CANALIZACIÓN

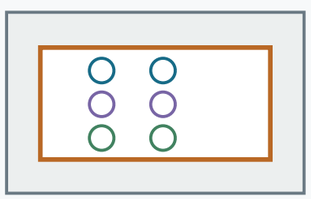

Ducto existente / propuesto*: trazado esquemático

3 cables independientes OS2 24F, E1–E3

Registros, entradas y reservas: ubicación teórica

*** Supuesto de diseño; no es una medición de campo.**

LONGITUDES Y ALCANCE DEL ESCENARIO

E1: (145 + 50 + 16) × 1,05 = 221,55 m de cable.

E2: (145 + 75 + 16) × 1,05 = 247,80 m de cable.

E3: (50 + 16) × 1,05 = 69,30 m de cable.

145 m reportados; 50 m y distancias de escenario por verificar.

OS2 24F exterior; OS2 12F vertical (ver láminas 06–09).

PROYECTO: INA CENATE | ELTT12000 | CABLEADO ESTRUCTURADO	FECHA 2026-10-29	REV. C	LÁMINA 01/09
Longitudes de escenario, no mediciones. Geometría, registros y reservas sujetos a verificación en campo.	SIN ESCALA	IA: apoyo visual	NO CONSTRUCTIVO