
# CANASTAS Y TUBERÍAS · EDIFICIO B




Planta académica típica · 6 laboratorios de 75 m² supuestos · bandeja 100 × 50 mm · tubo nominal Ø25 mm

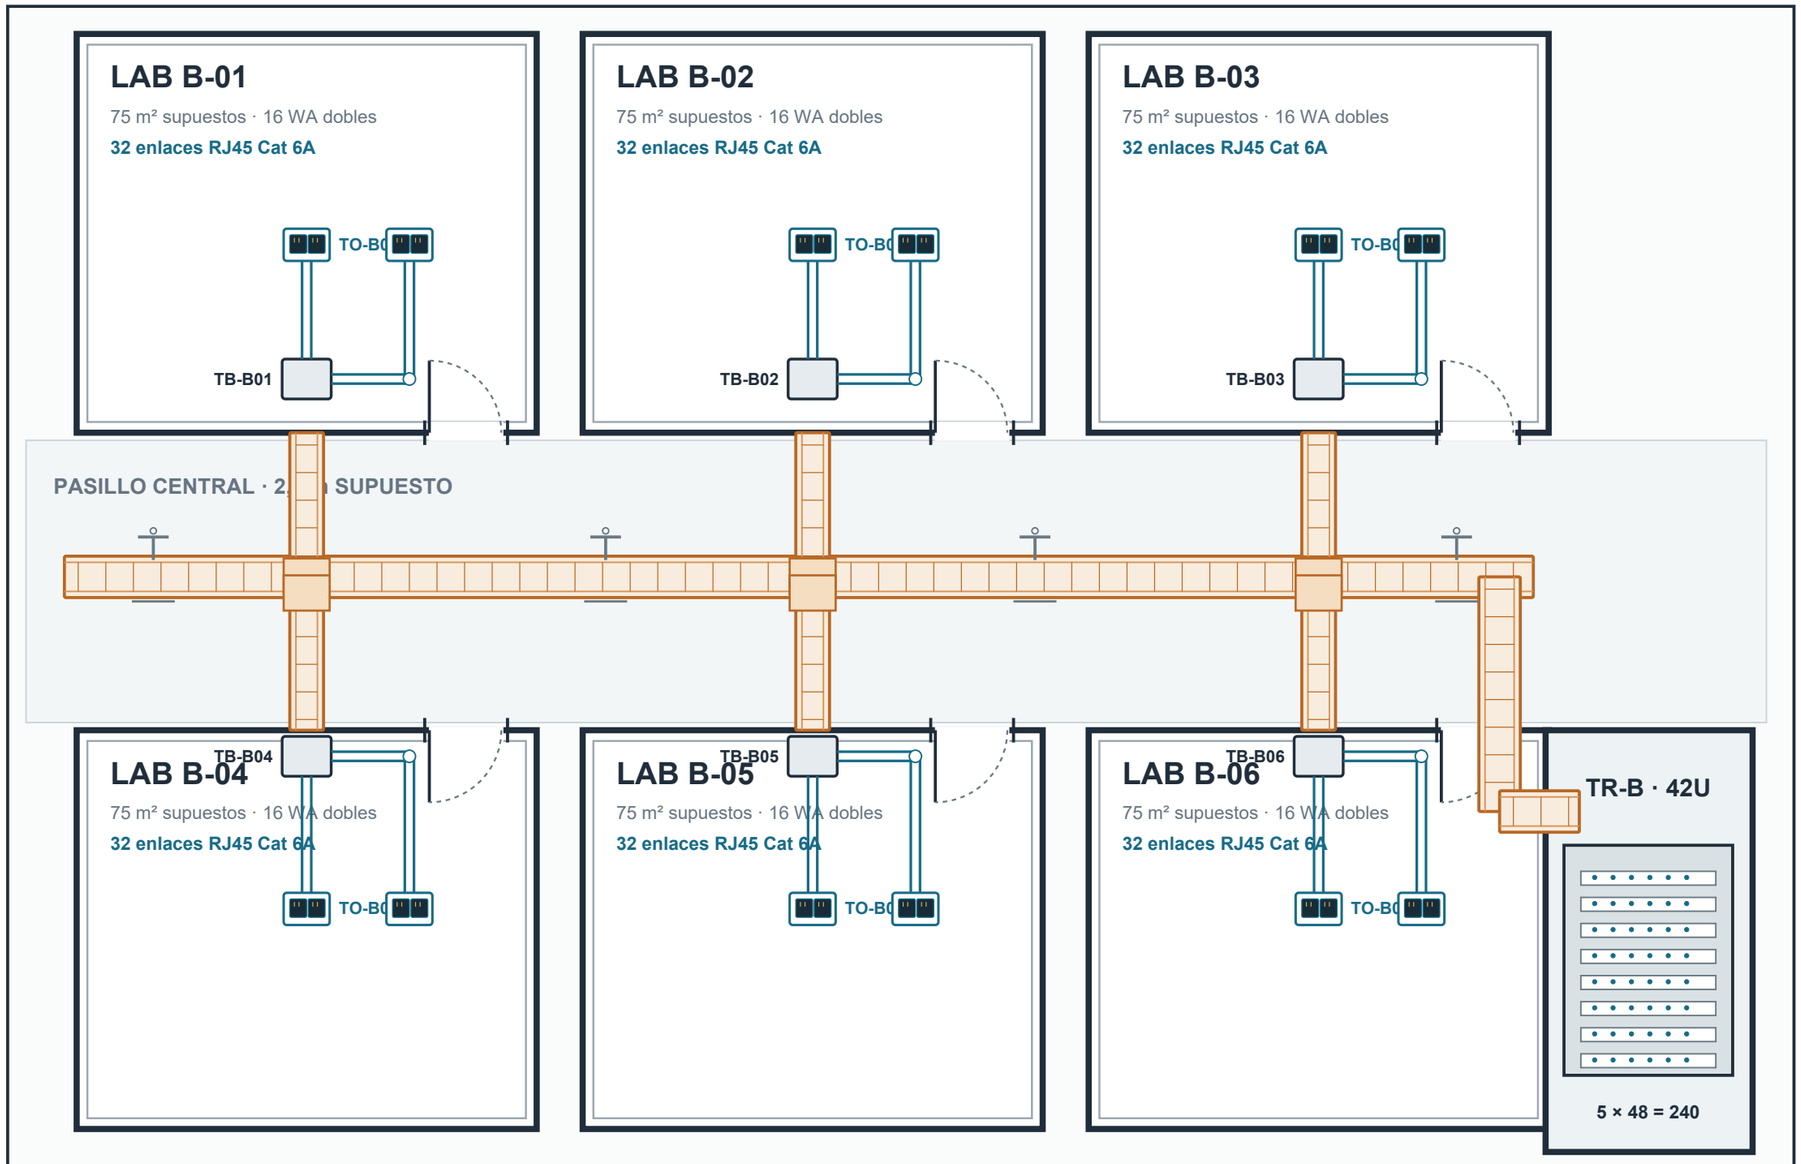



Rutas, muros, soportes y salidas ilustrativos. 2 salidas por lab dibujadas como muestra; no equivalen a las 16 WA.

**6 laboratorios × 16 WA dobles × 2 RJ45 = 192 enlaces Cat 6A por piso; TR-B: 5 × 48 = 240 posiciones.**

## DETALLE · TRANSICIÓN

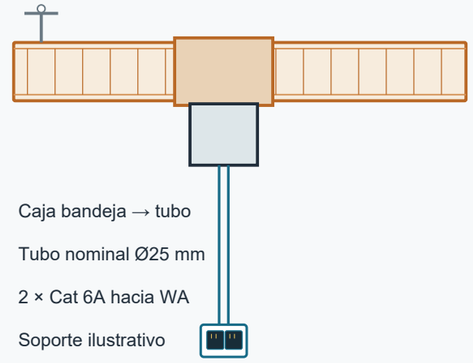


## DETALLE · SALIDA DOBLE

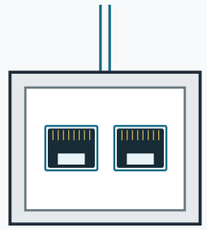

2 × RJ45 Cat 6A

## LEYENDA

- Bandeja 100 × 50
- Tubo nominal Ø25
- WA doble / 2 RJ45
- Transición / caja

| PROYECTO: INA CENATE \| ELTT12000 \| CABLEADO ESTRUCTURADO | FECHA 2026-10-29 | REV. C | LÁMINA 03/09 |
|---|---|---|---|
| Geometría y recorridos supuestos; confirmar instalación, fijaciones y ocupación antes de construir. | SIN ESCALA | IA: apoyo visual | NO CONSTRUCTIVO |