
# ÁREAS DE TRABAJO · EDIFICIO B

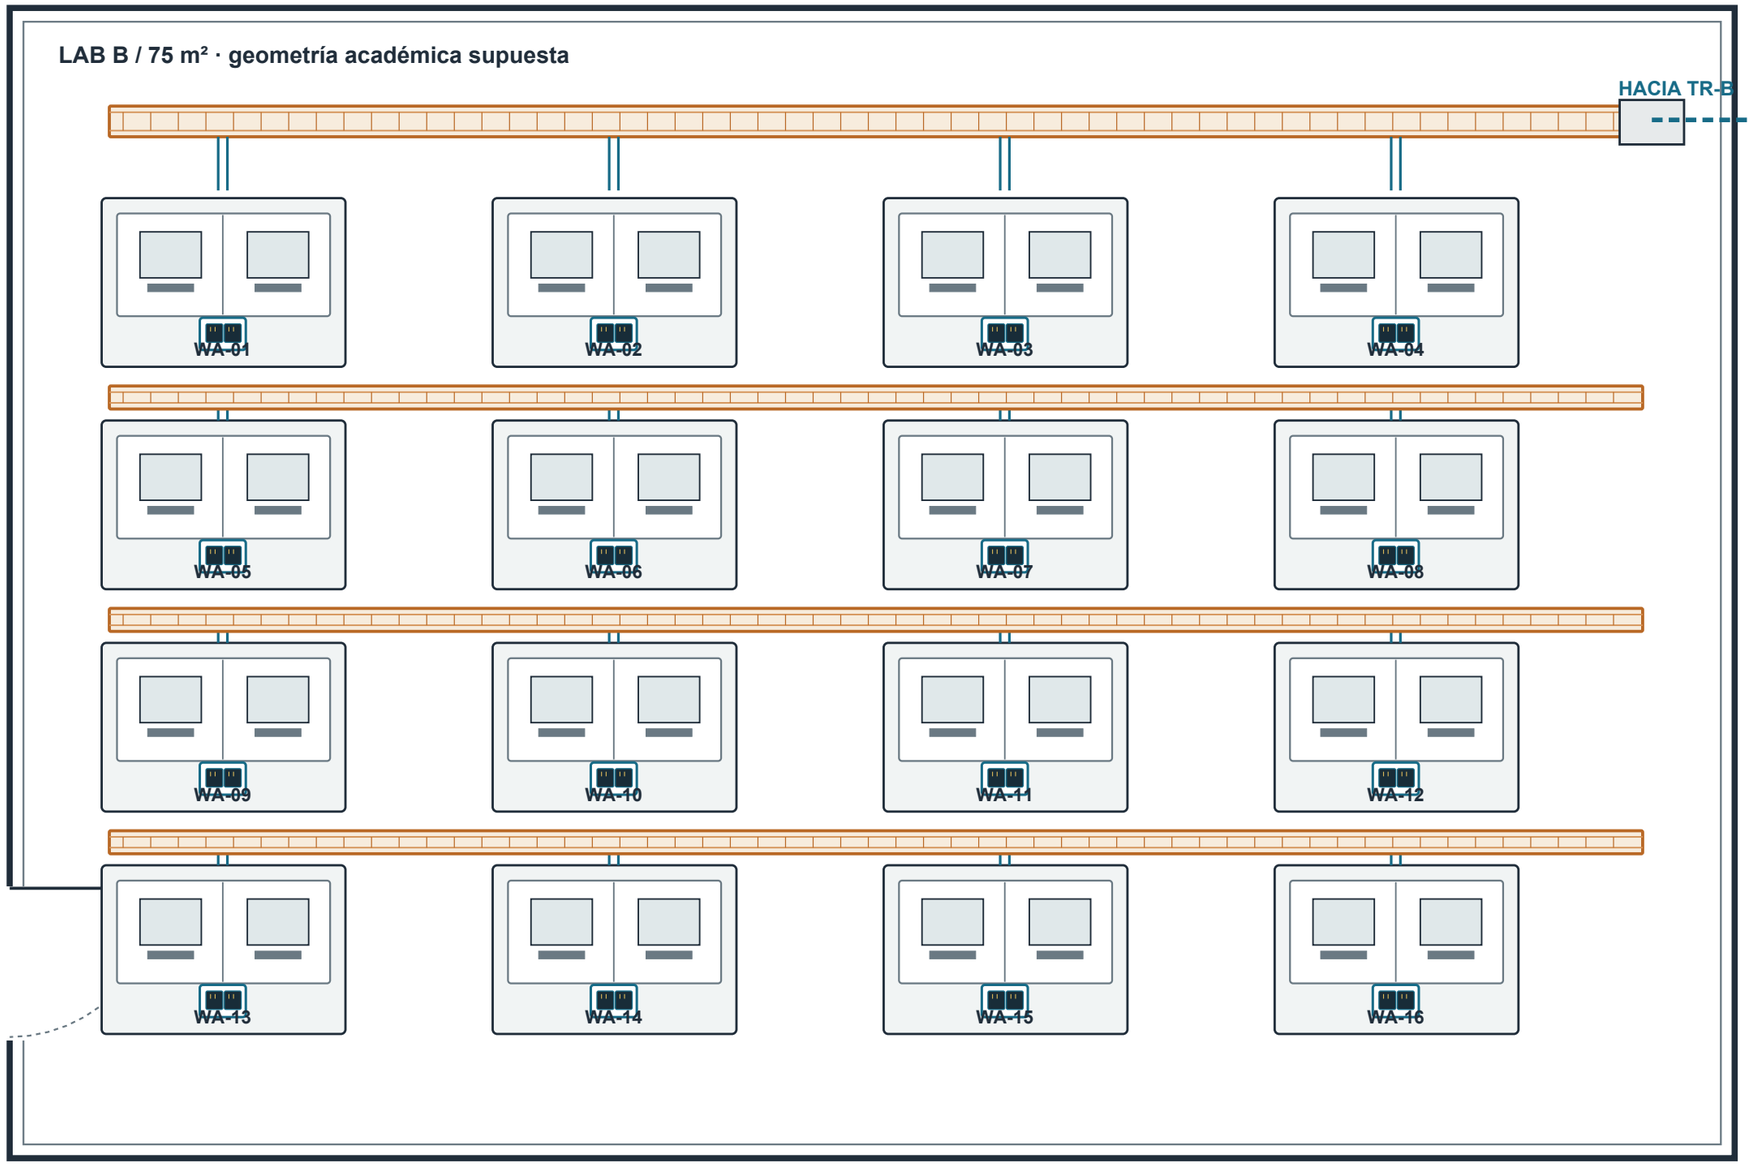


Laboratorio típico 75 m² · 16 WA dobles · 32 puertos RJ45 Cat 6A · planta y mobiliario supuestos




16 placas dobles identificadas WA-01–WA-16; cada símbolo muestra 2 bocas RJ45; 32 enlaces permanentes Cat 6A.

## DETALLE · PUESTO DOBLE

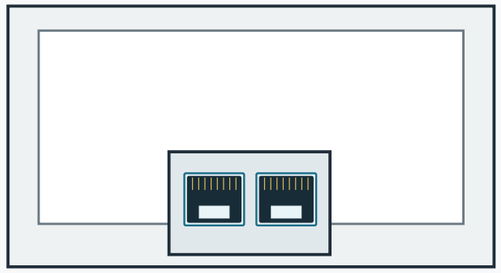


Placa, caja y conectores ilustrativos.

**2 cables Cat 6A por WA; ruta agrupada.**

## RUTA Y LEYENDA

- Bandeja de distribución*
- Tubería nominal Ø25*
- WA doble · 2 × RJ45
- Cat 6A permanente

Ruta agrupada hacia TR; no se dibujan 32 cables individuales superpuestos.

* Posición y recorrido supuestos.

Escala: esquemático, sin escala.

| PROYECTO: INA CENATE \| ELTT12000 \| CABLEADO ESTRUCTURADO | FECHA 2026-10-29 | REV. C | LÁMINA 05/09 |
|---|---|---|---|
| 16 WA dobles × 2 RJ45 = 32 salidas por laboratorio. Mobiliario y canalizaciones supuestos. | SIN ESCALA | IA: apoyo visual | NO CONSTRUCTIVO |