BACKBONE EXTERIOR

Tres edificios · tres enlaces independientes · canalización y longitud de escenario

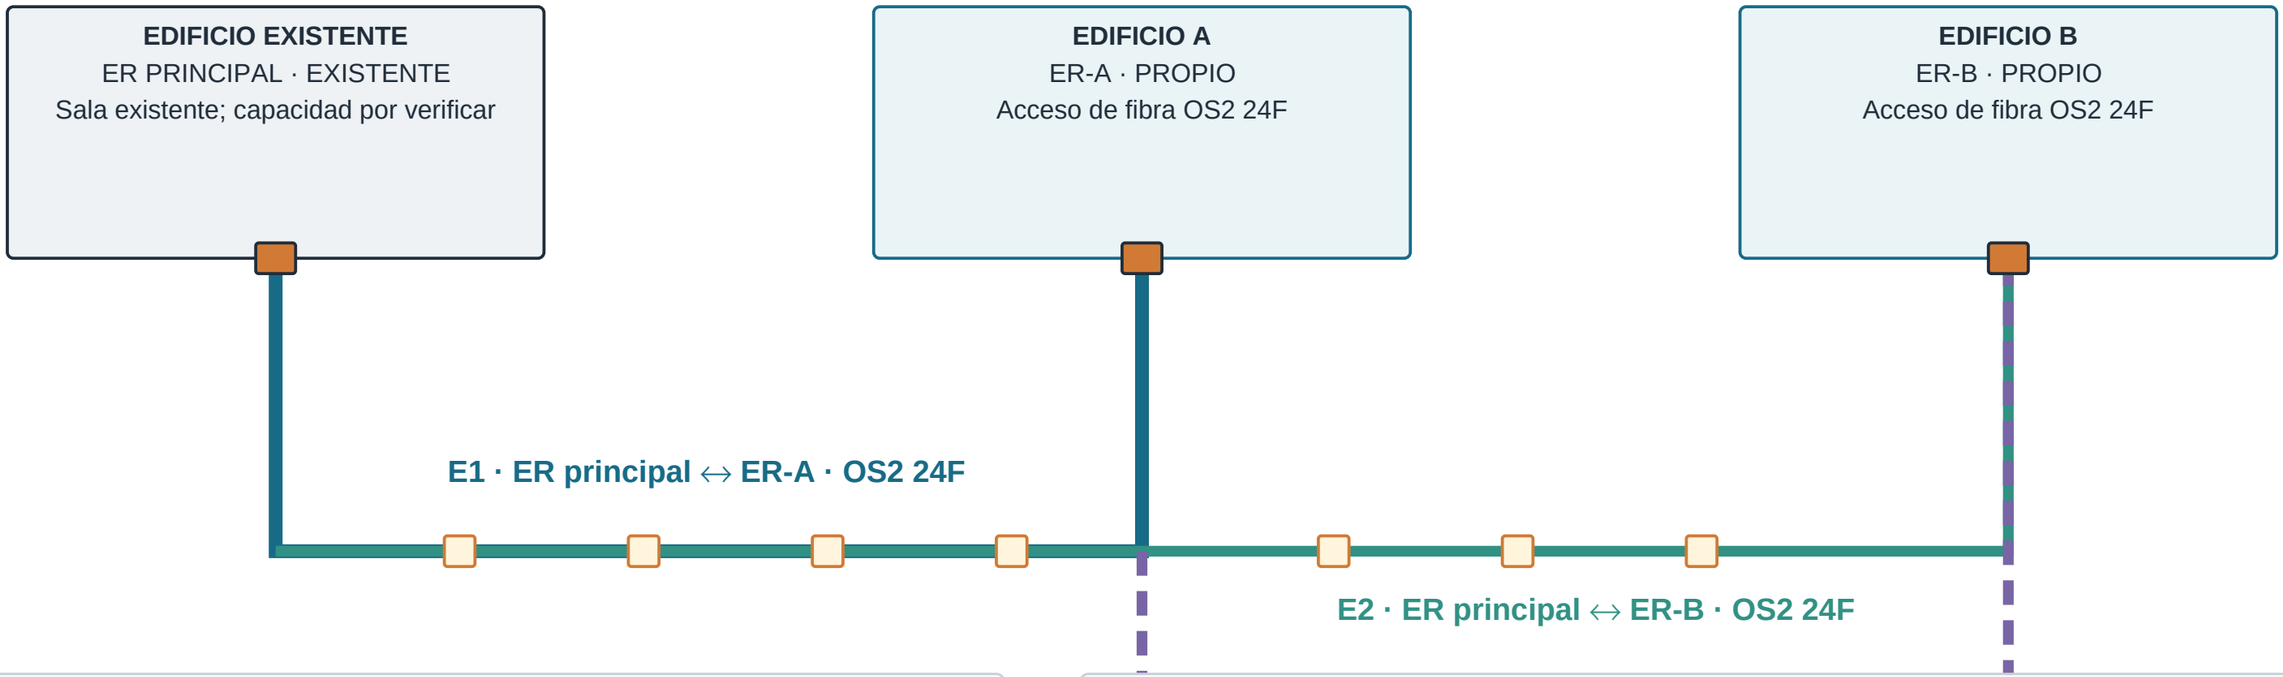

LONGITUDES DE ESCENARIO — NO SON MEDICIONES

E1 cable: 221,55 m = (145 + 50 + 16) × 1,05

E2 cable: 247,80 m = (145 + 75 + 16) × 1,05

E3 cable: 69,30 m = (50 + 16) × 1,05

145 m reportados; 50 m propuestos; x=75 m e y=50 m supuestos.

Ducto común 145 m + extensión a A 50 m: condición por validar.

Los 16 m cubren entradas y reservas del escenario; 5 % desperdicio.

SÍMBOLOS Y CONDICIONES

OS2 24F · E1

OS2 24F · E2

OS2 24F · E3

Registro teórico, ubicación/cantidad sin validar en campo

Canalización subterránea existente / nueva: trazado esquemático, condición pendiente.

PROYECTO: INA CENATE | ELTT12000 | CABLEADO ESTRUCTURADO	**FECHA 2026-10-28**	**REV. 0**	**LÁMINA 01/09**
Recorridos, registros, ductos y entradas requieren levantamiento; longitudes de cable son resultados del escenario.	**SIN ESCALA**	IA: apoyo visual	**NO CONSTRUCTIVO**