
CANALIZACIONES EDIFICIO A

Planta académica típica: 5 laboratorios / TR-A · bandeja 100 × 50 mm · tubo nominal Ø25 mm

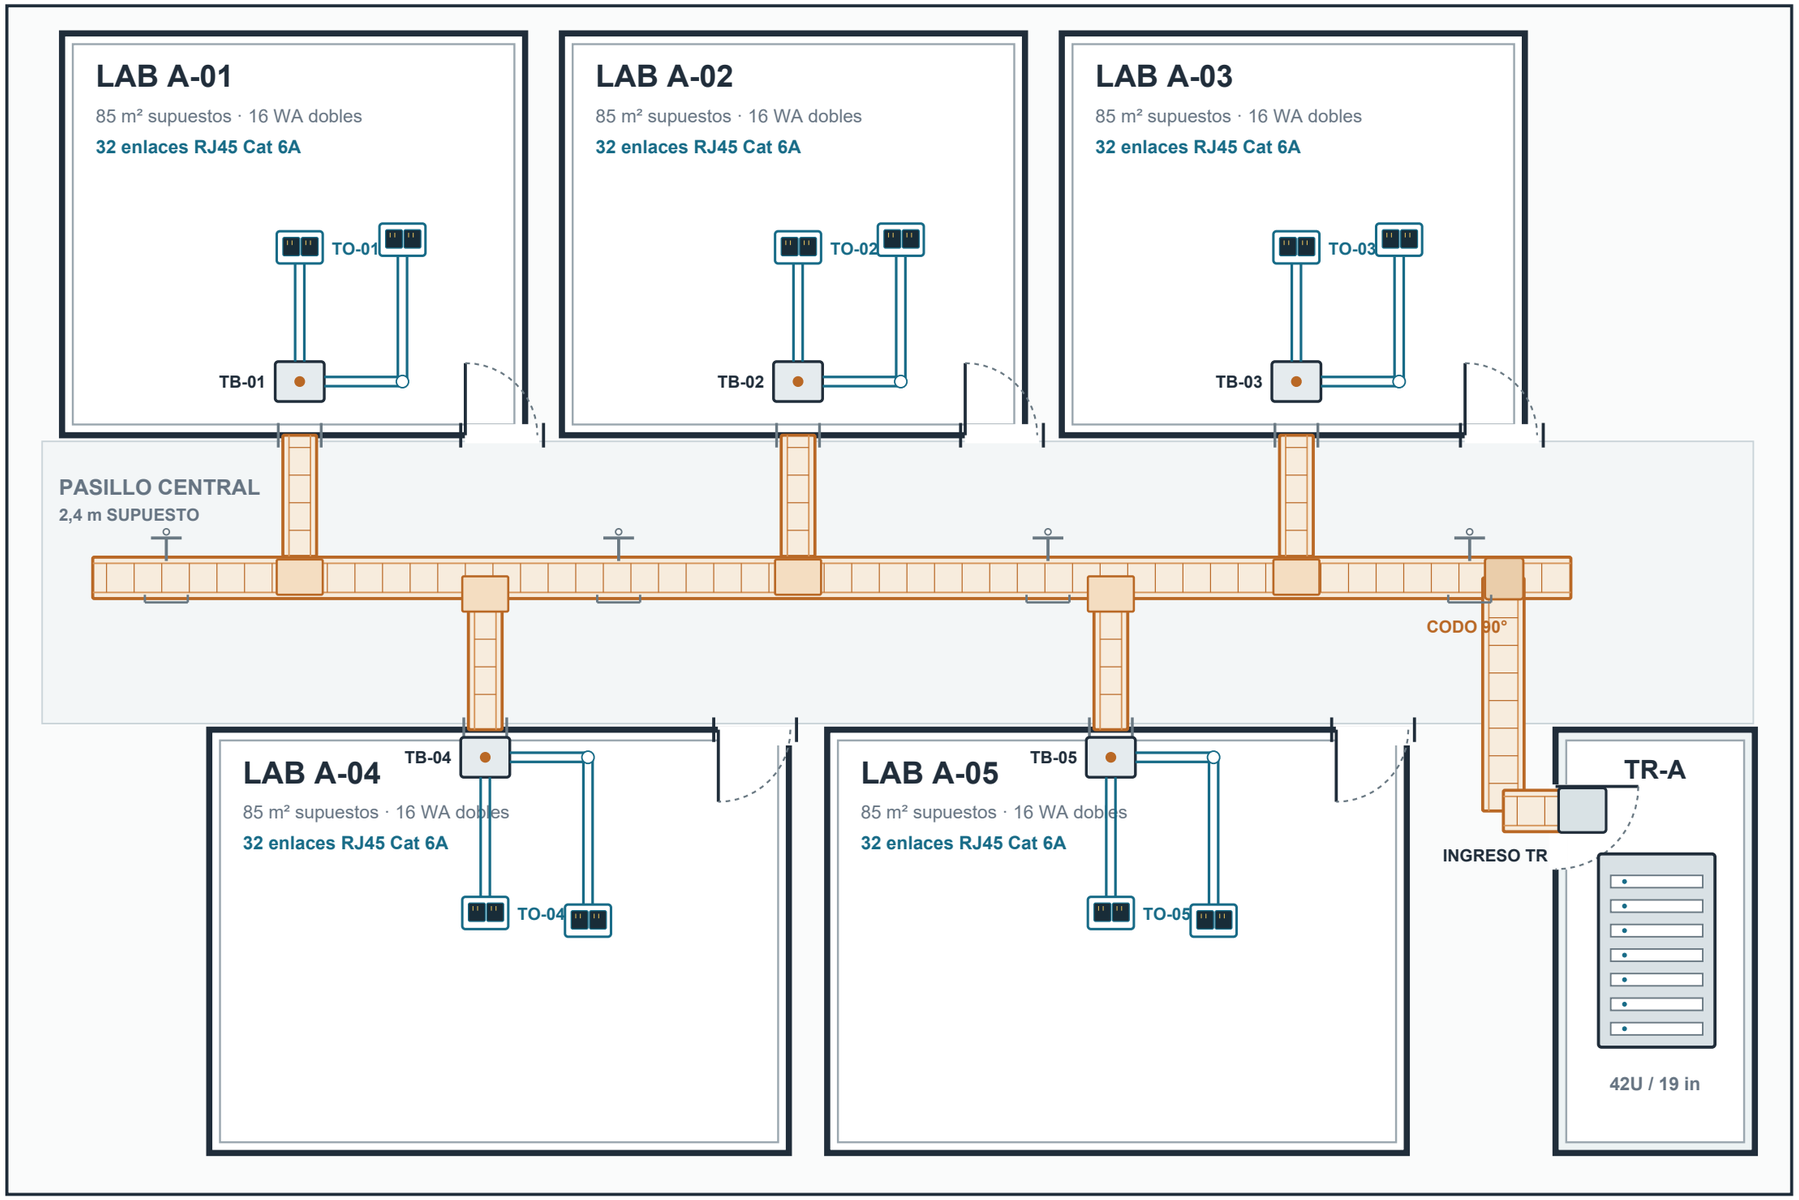


Rutas, muros y pasamuros supuestos. Dos salidas por laboratorio ilustran la distribución; no son las 16 WA completas.

Cada laboratorio: 16 WA dobles × 2 RJ45 = 32 enlaces. TR-A: 5 × 32 = 160 enlaces Cat 6A.


DETALLE A · TRANSICIÓN

Bandeja 100 × 50 mm

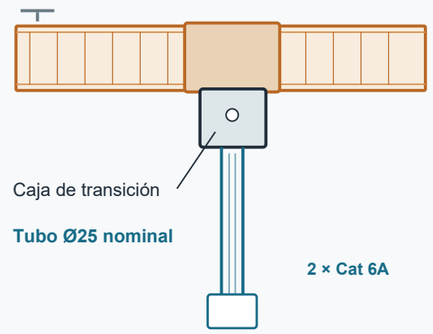

Soporte y fijación ilustrativos

DETALLE B · SALIDA DOBLE

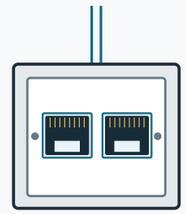

WA doble · 2 × RJ45 Cat 6A

Placa / caja de salida ilustrativa

LEYENDA DE CANALIZACIÓN

- Bandeja aérea · 100 × 50 mm
- Tubo nominal Ø25 mm
- Caja de transición a tubo
- Salida doble RJ45
- Cableado Cat 6A permanente

PROYECTO: INA CENATE | ELTT12000 | CABLEADO ESTRUCTURADO	**FECHA 2026-10-29**	**REV. C**	**LÁMINA 02/09**
recorridos, ubicación de salidas y fijaciones ilustrativos; verificar en campo.	**SIN ESCALA**	IA: apoyo visual	**NO CONSTRUCTIVO**